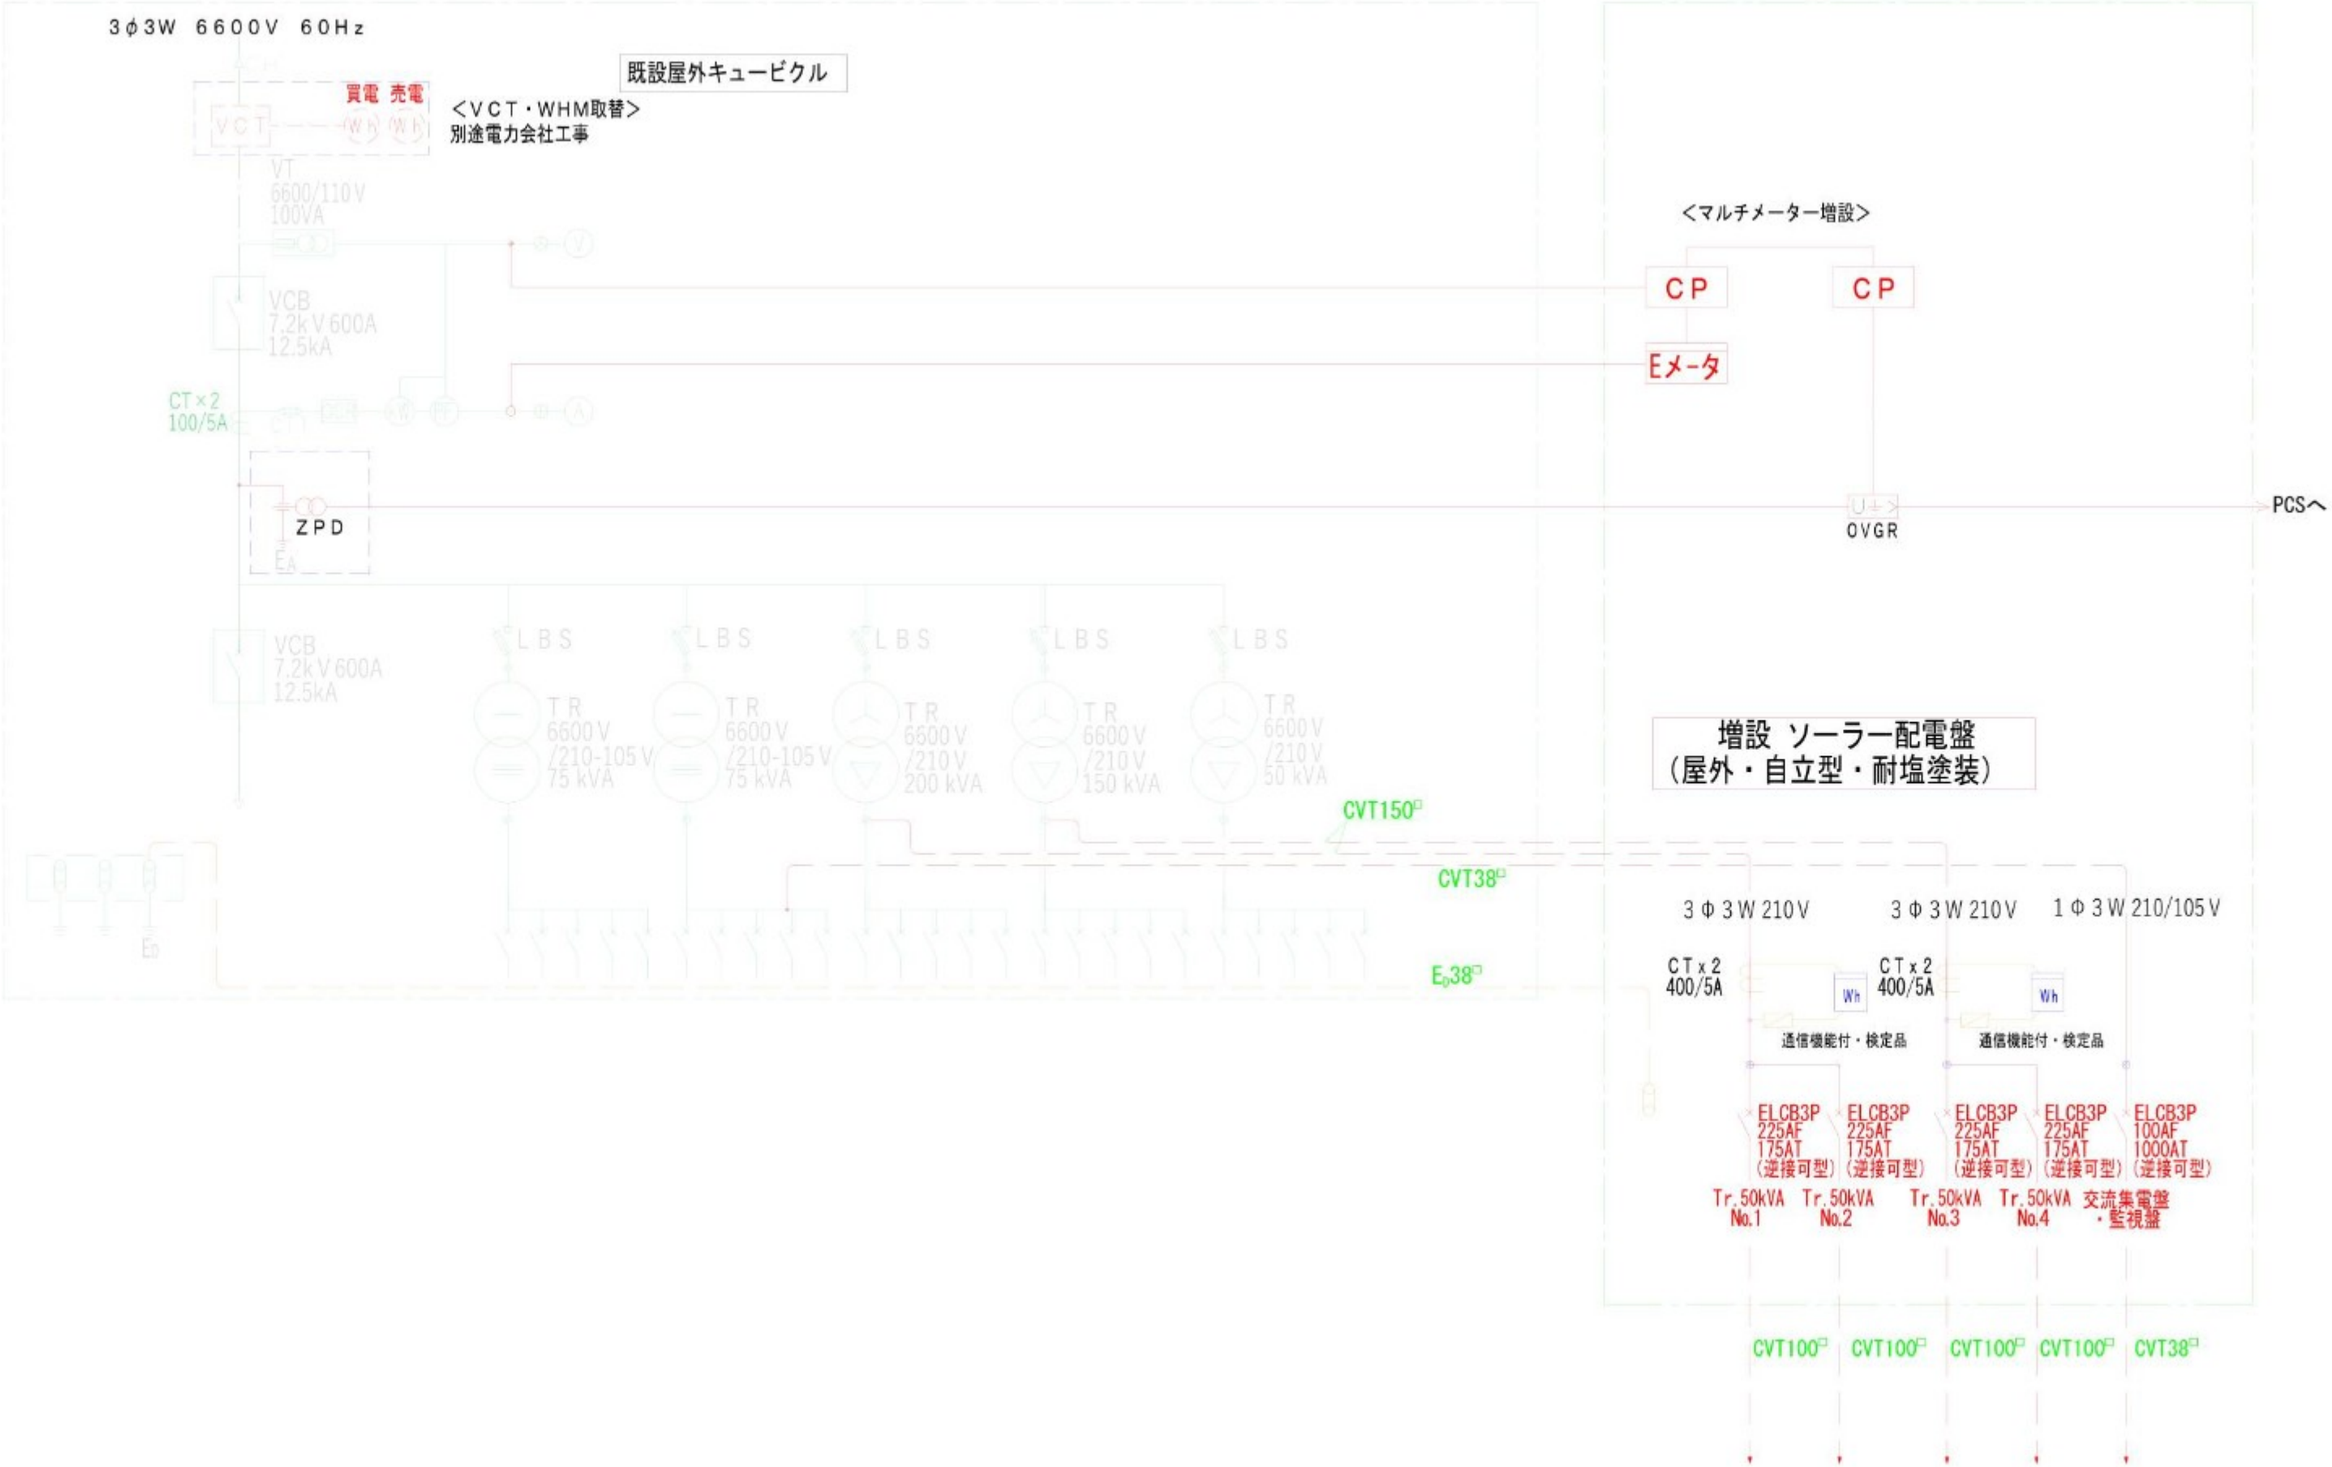

PLOTTER	CHECK	PROJECT	TITLE	SCALE	DATE	NO
	[redacted]	[redacted] 太陽光発電設置工事	単線結線図(1)	–	2023.03	01

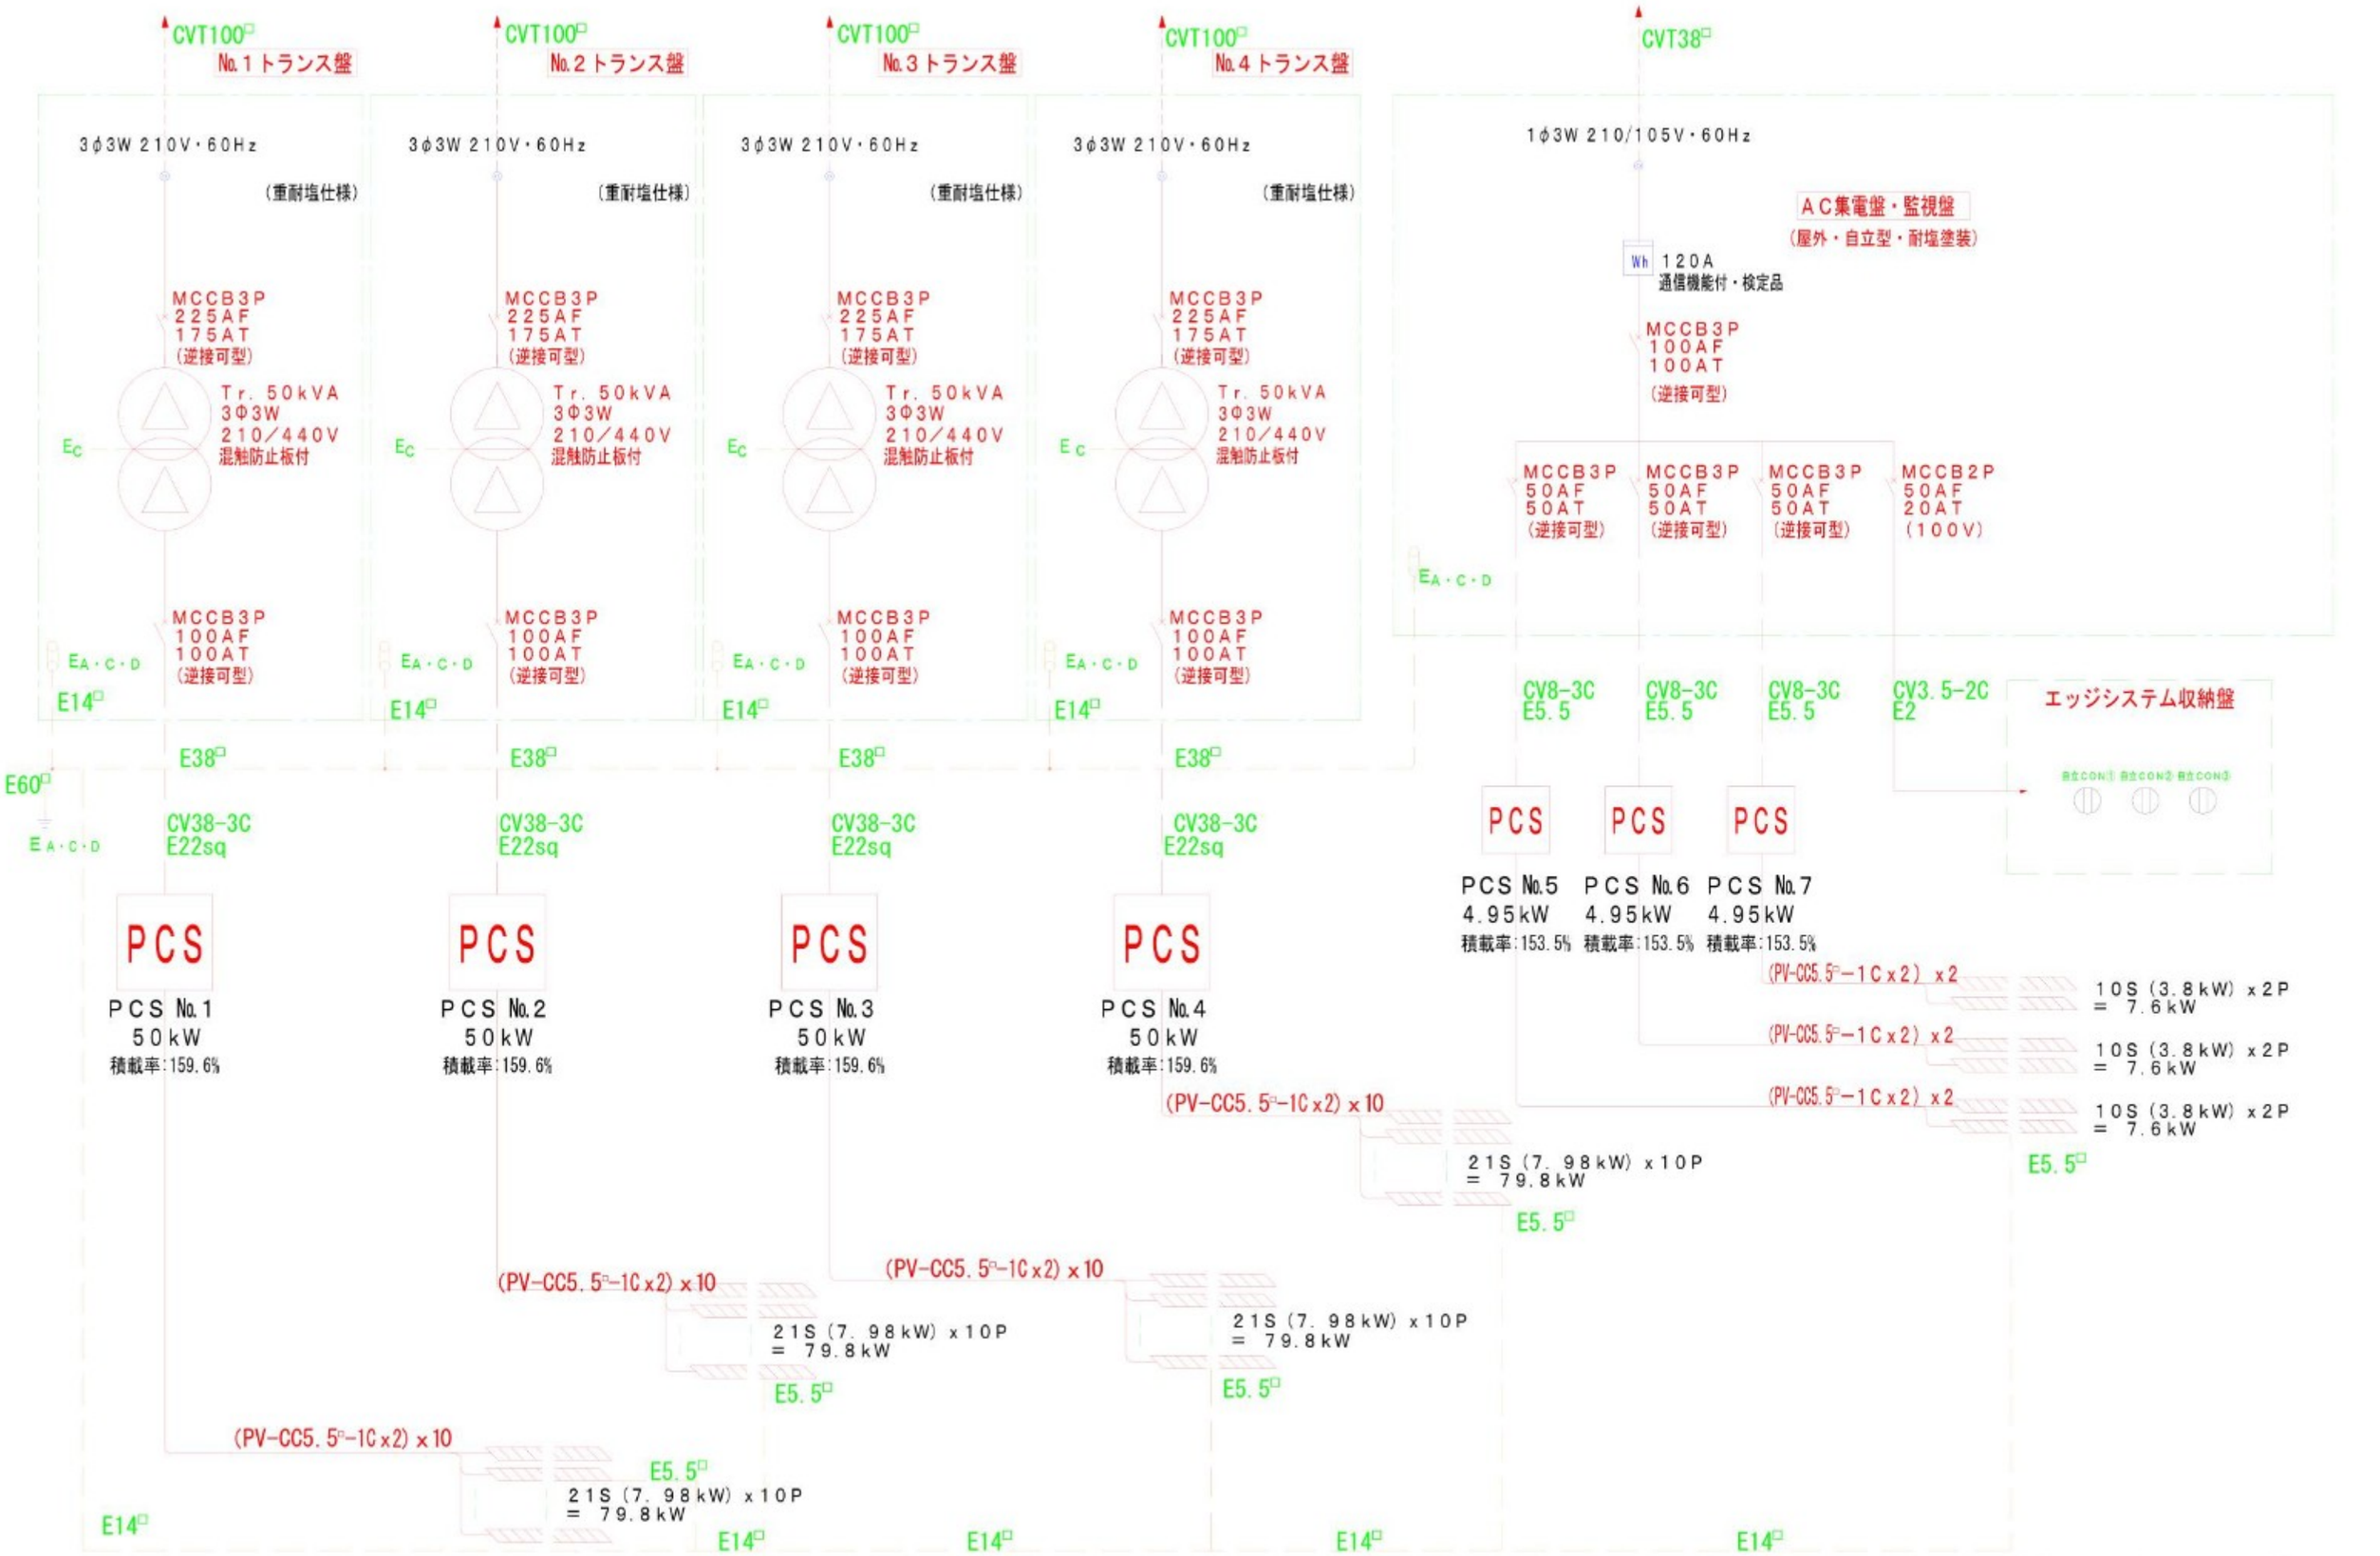

PLOTTER	CHECK	PROJECT	TITLE	SCALE	DATE	NO
	[redacted]	[redacted] 太陽光発電設置工事	単線結線図(2)	-	2023.03	02

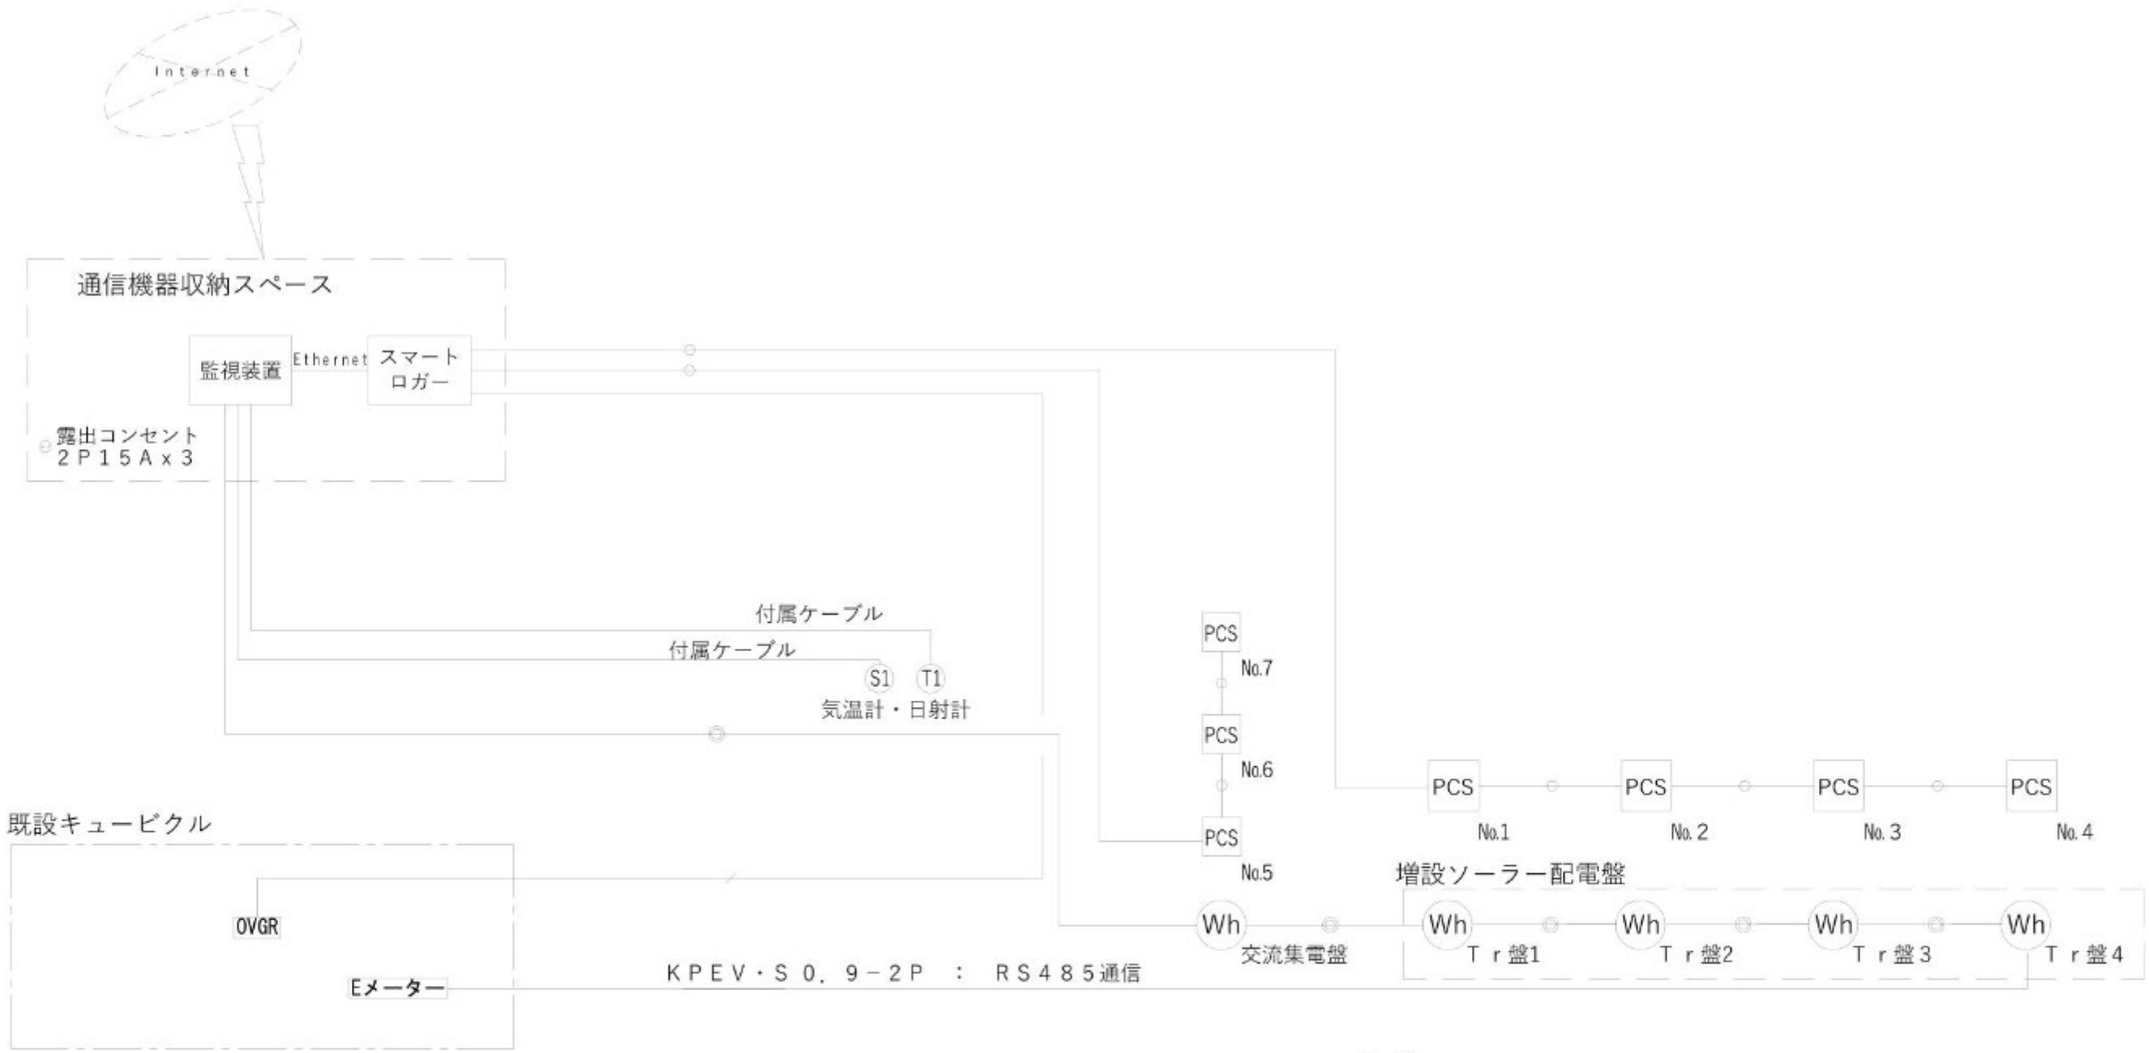

凡 例

- ＫＰＥＶ・Ｓ１．２５－１Ｐ　：　緊急停止（OVGR）
- ＫＰＥＶ・Ｓ０．９－２Ｐ　：　ＲＳ４８５通信（PCS）
- ＫＰＥＶ・Ｓ１．２５－２Ｐ　：　ＲＳ４８５通信

PLOTTER	CHECK		PROJECT	TITLE	SCALE	DATE	NO
		[redacted]	[redacted] 太陽光発電設置工事	通信・制御線系統図	－	2023.03	03